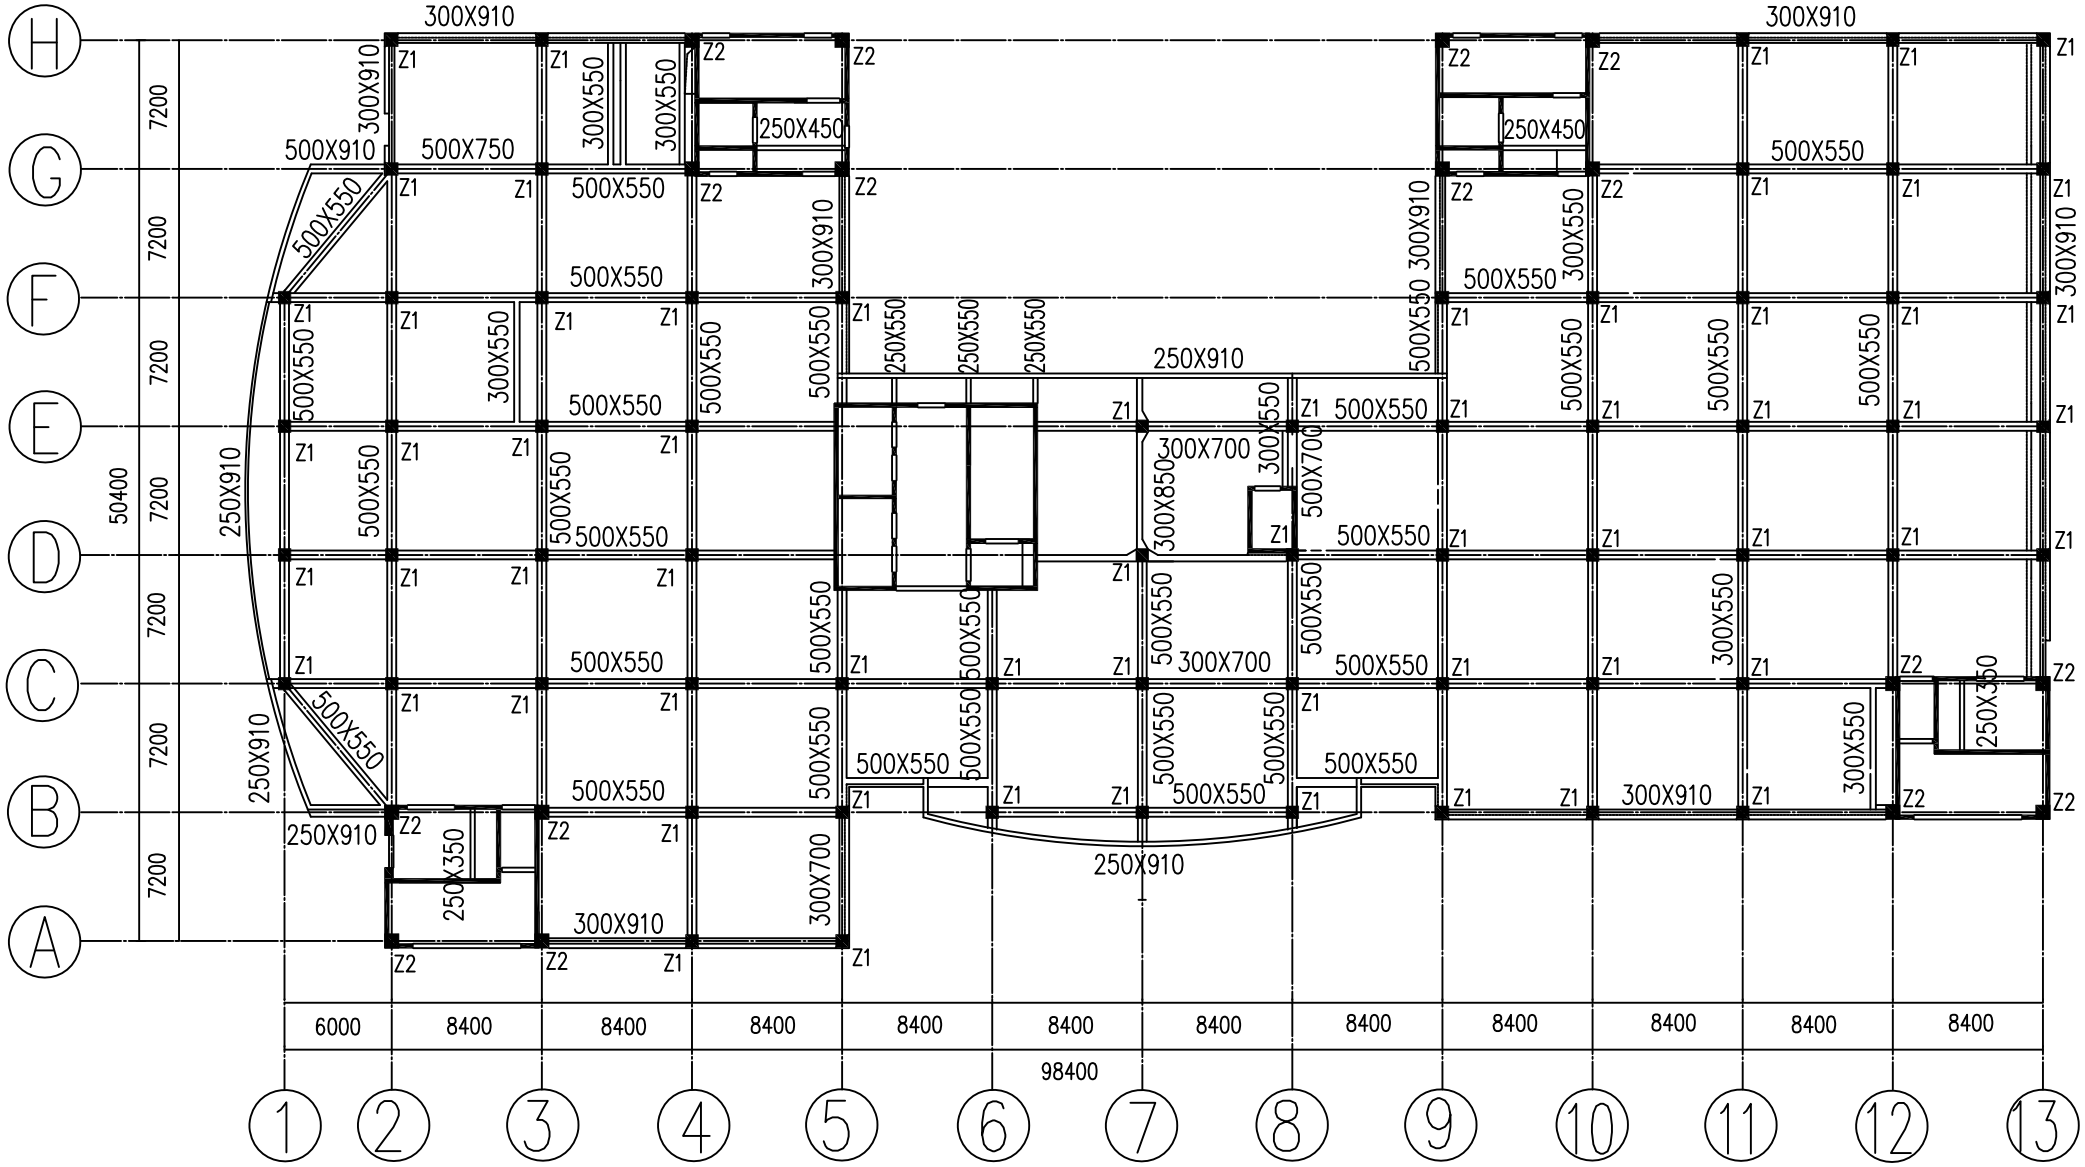

The strength of concrete is C30 (the compressive strength determined from the standard cube tests is 30 MPa)

The width of shear walls is 250 mm

Z1, Z2 : the section sizes of columns are 700*700, 800*800 mm^2